



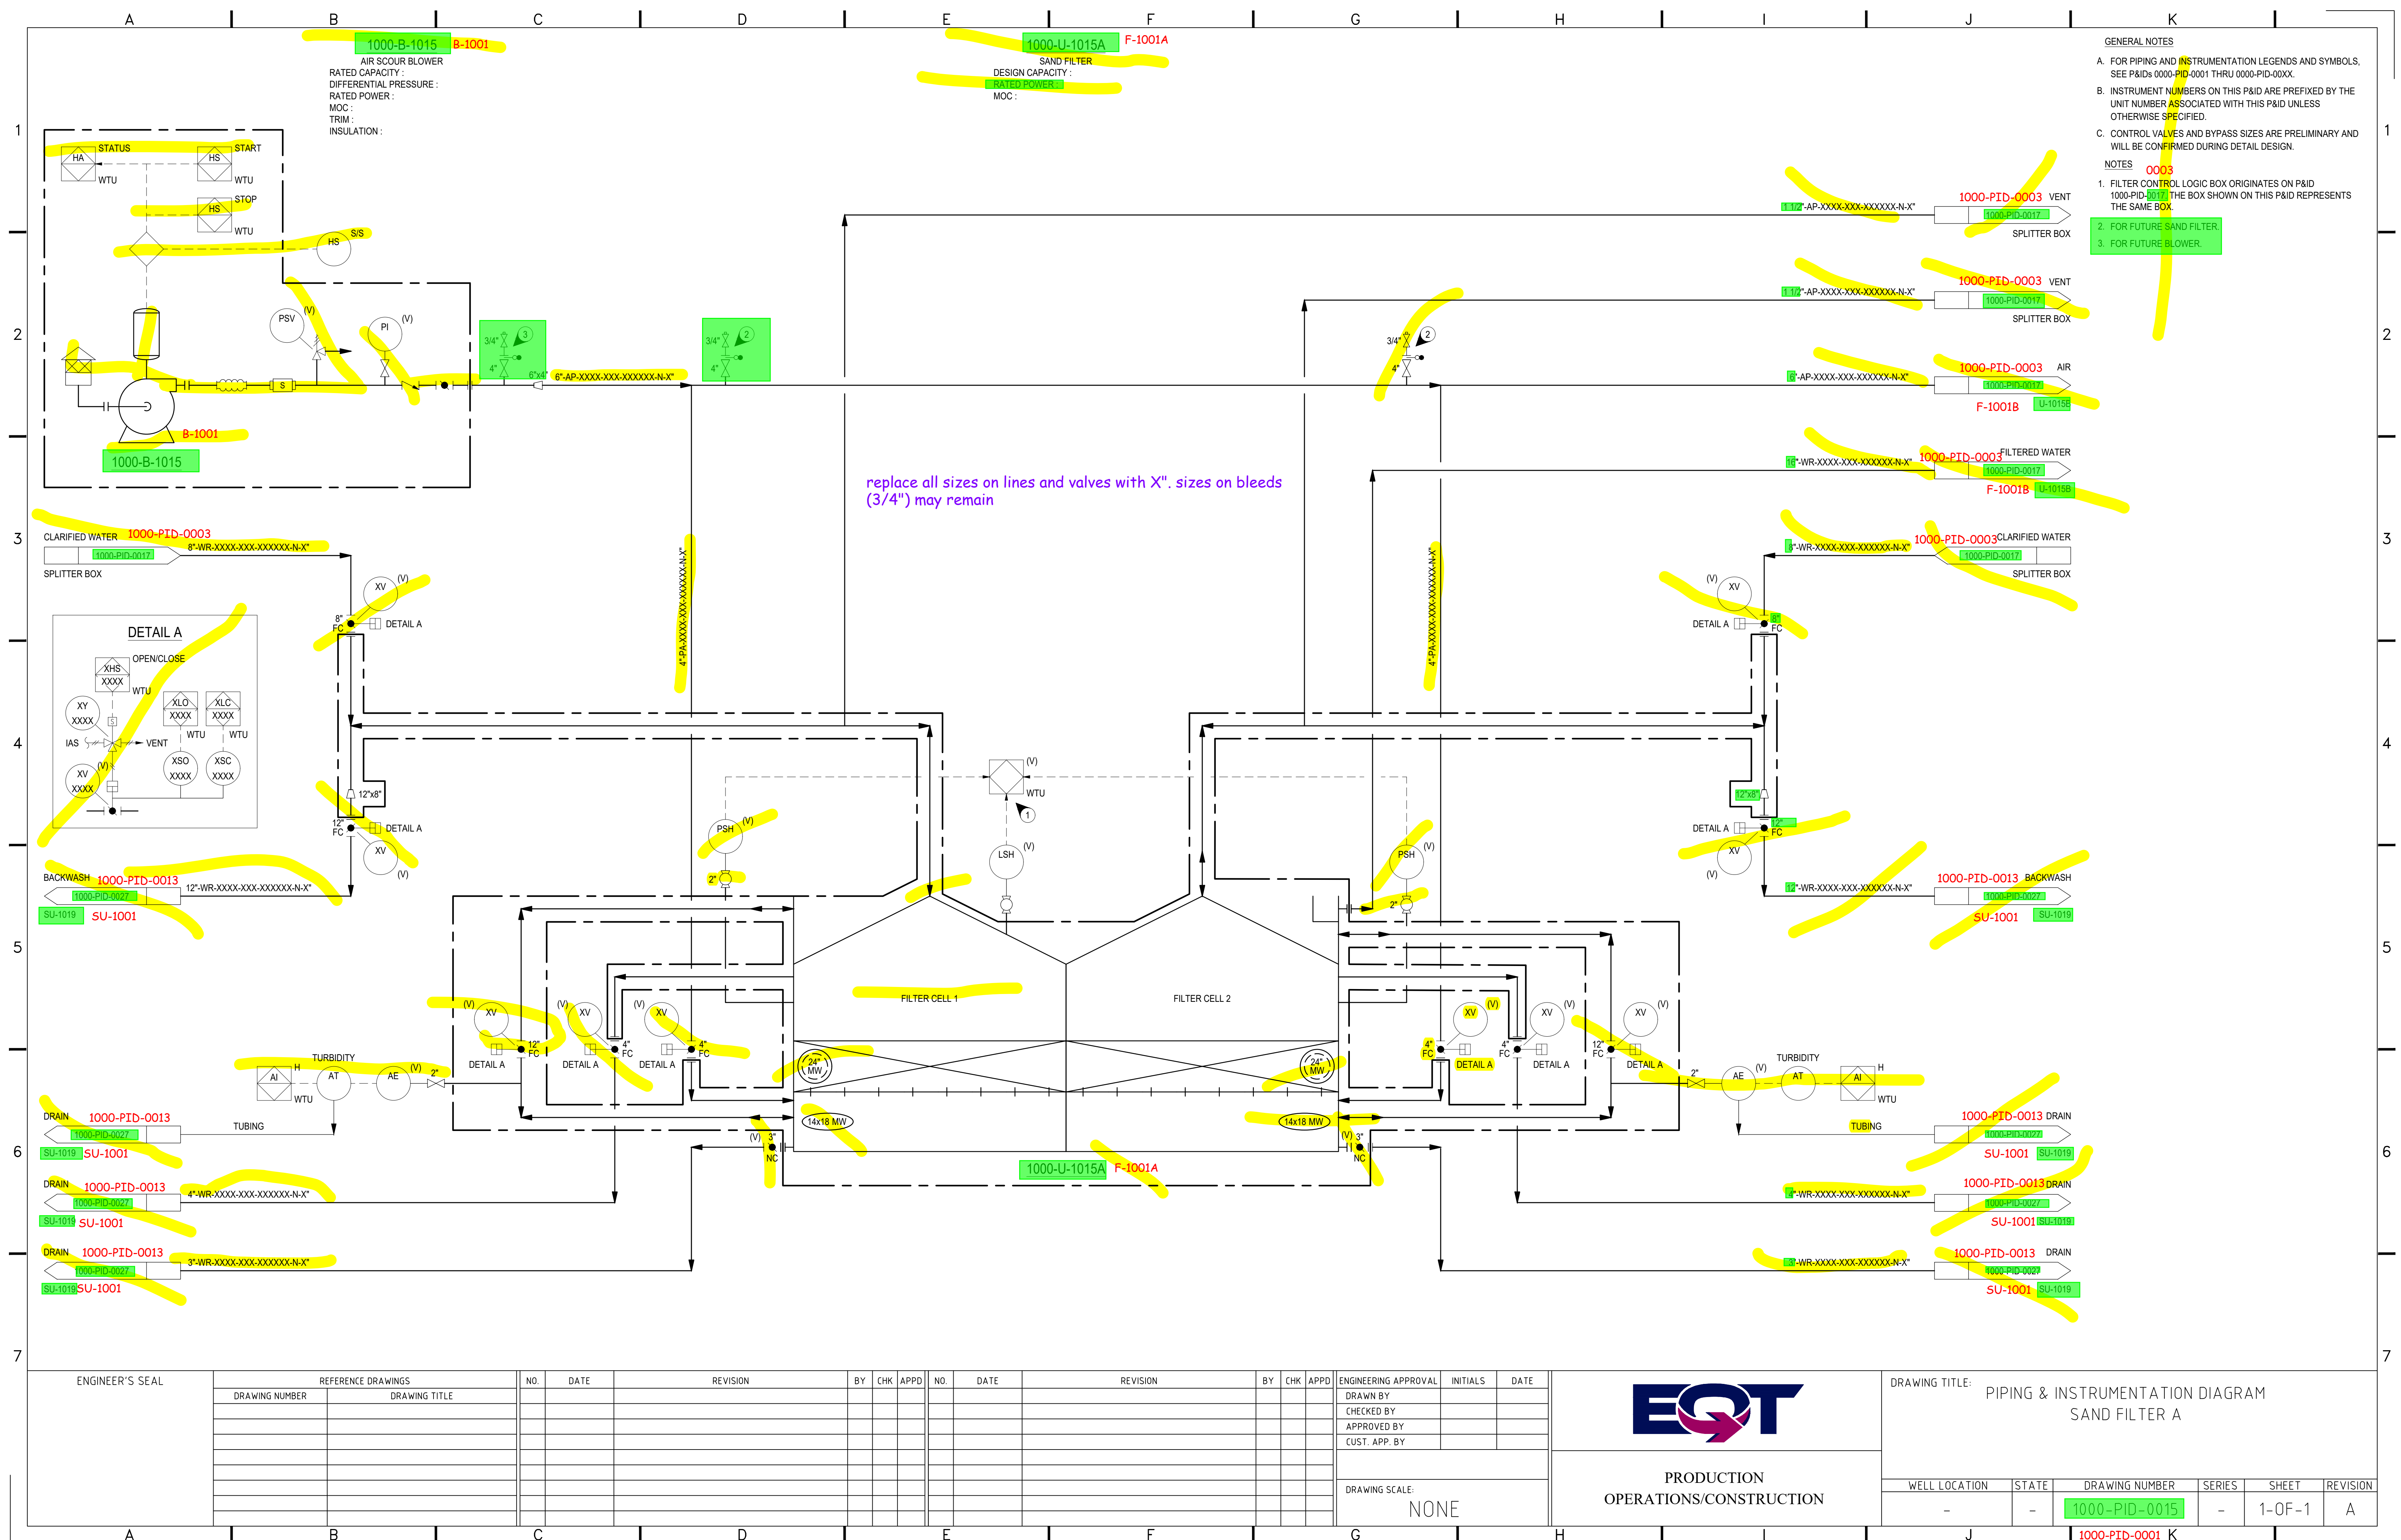

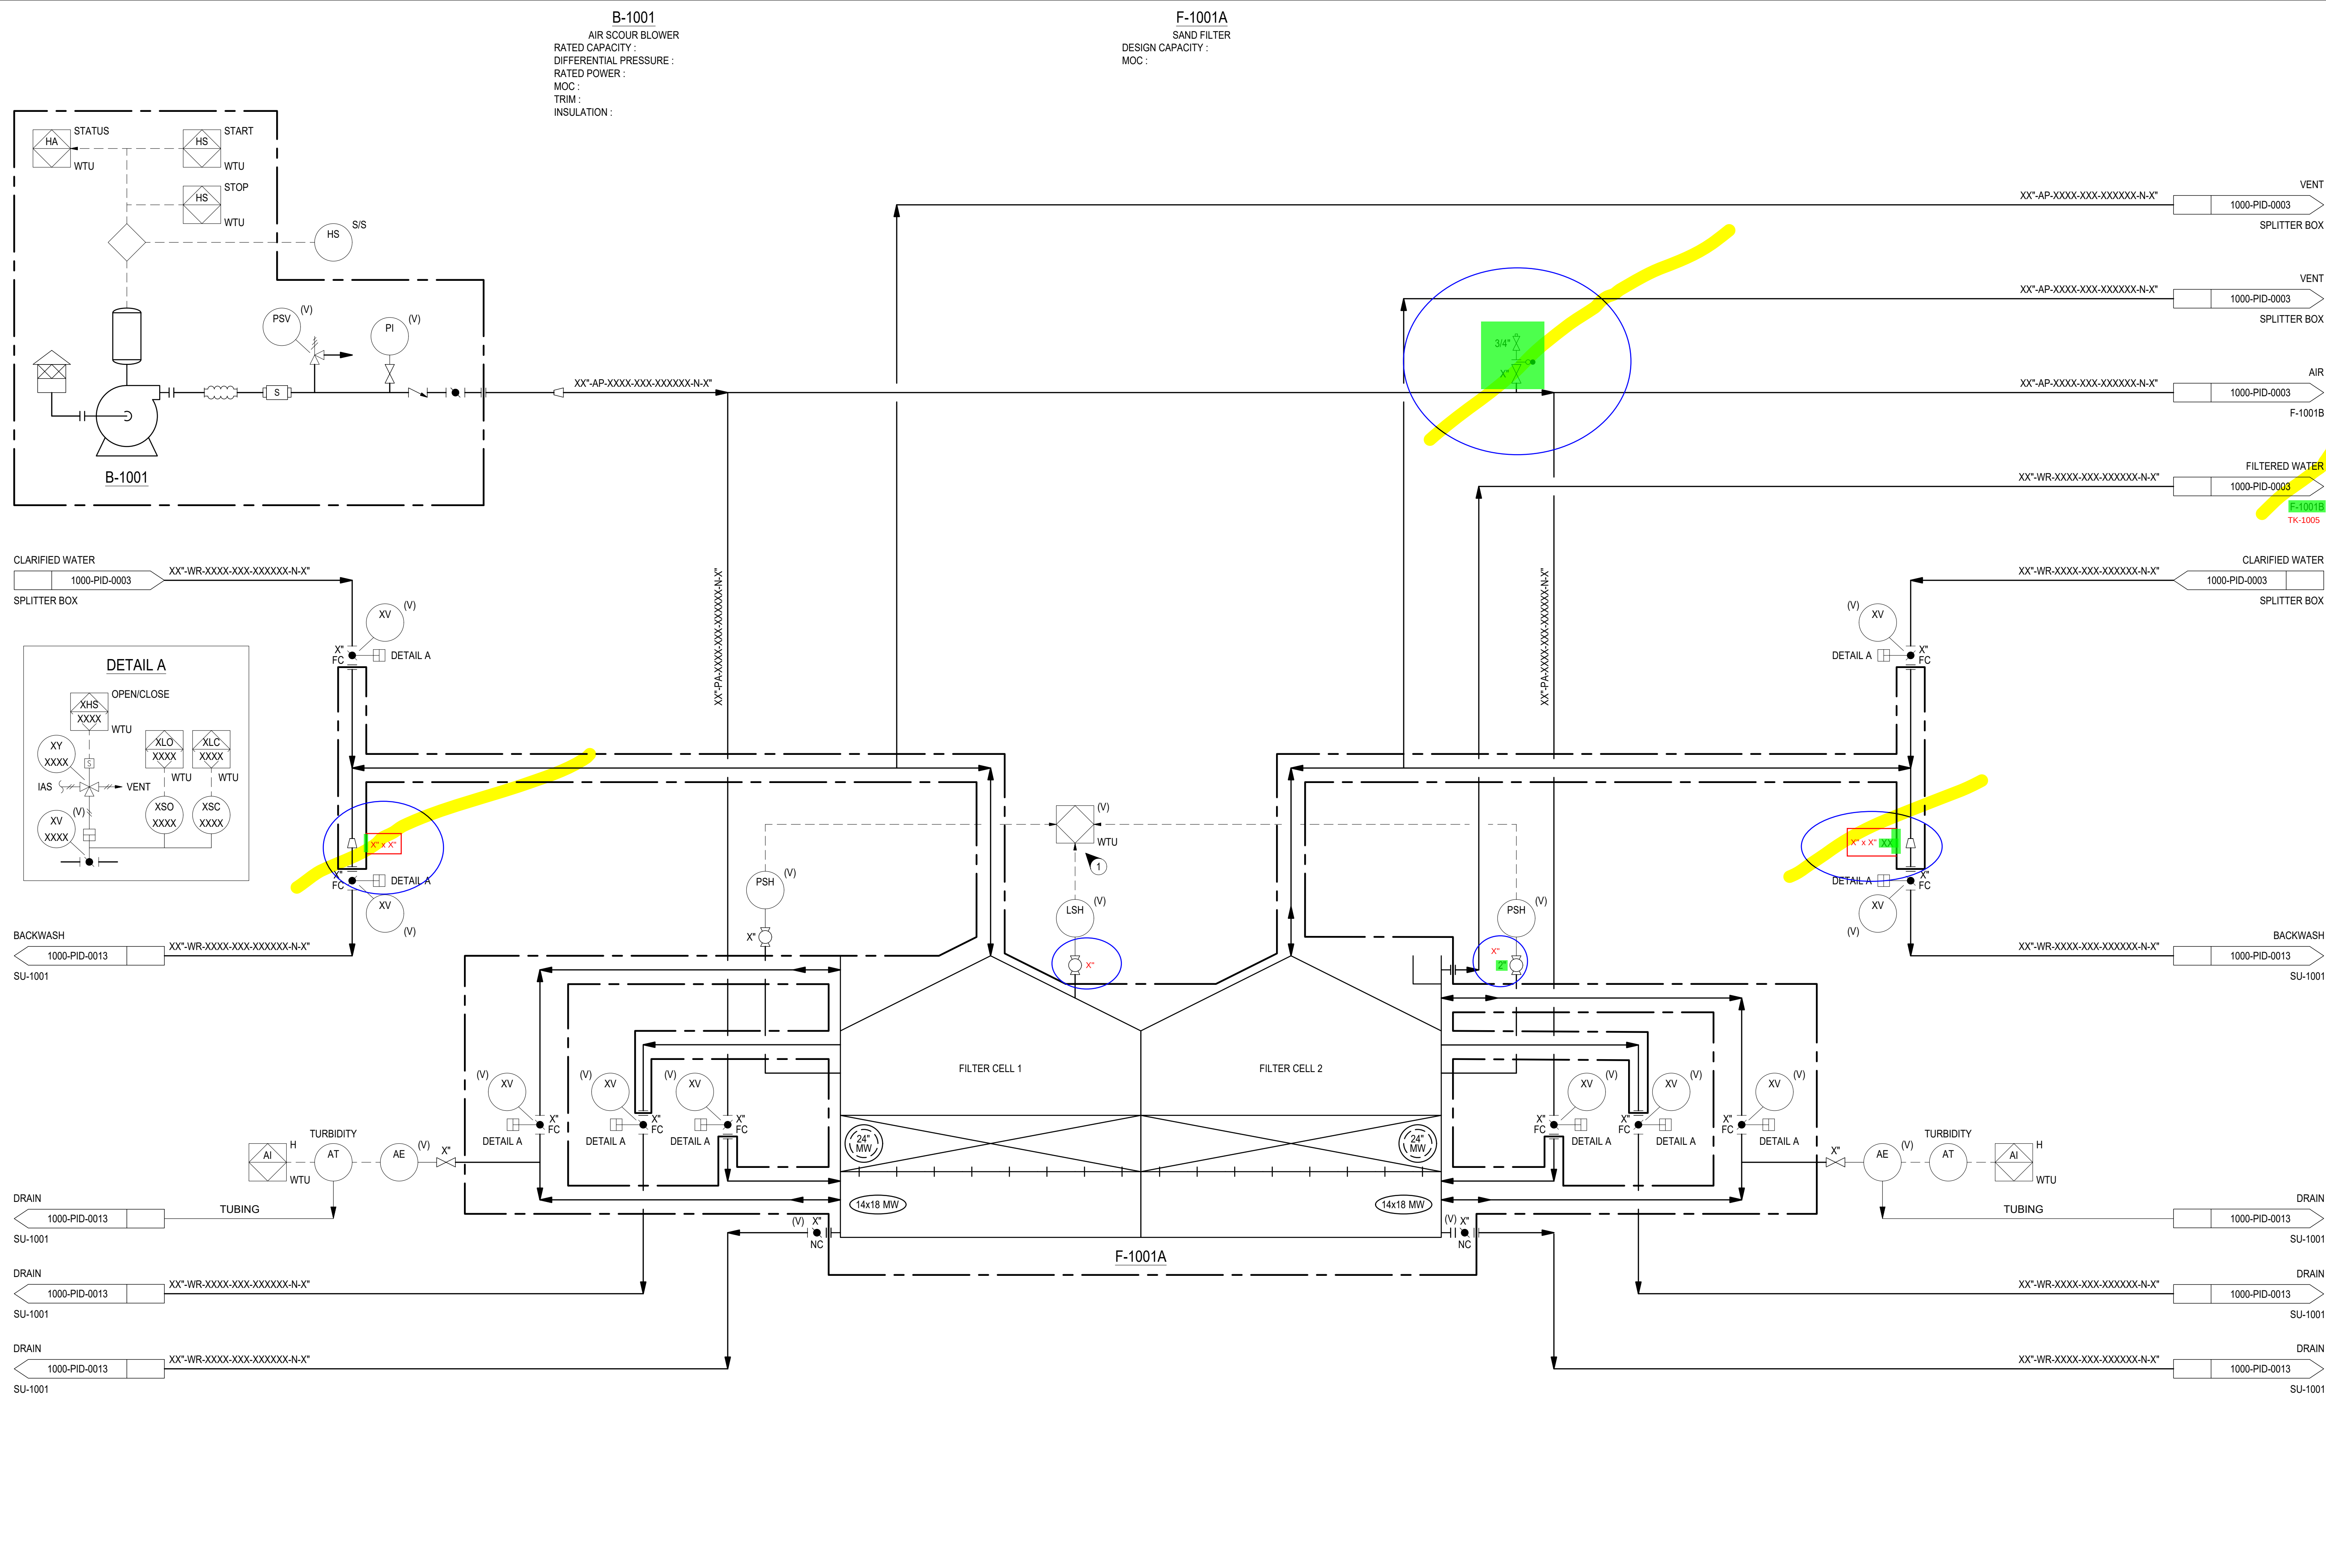

GENERAL NOTES

A. FOR PIPING AND INSTRUMENTATION LEGENDS AND SYMBOLS, SEE P&IDs 0000-PID-0001 THRU 0000-PID-00XX.

B. INSTRUMENT NUMBERS ON THIS P&ID ARE PREFIXED BY THE UNIT NUMBER ASSOCIATED WITH THIS P&ID UNLESS OTHERWISE SPECIFIED.

C. CONTROL VALVES AND BYPASS SIZES ARE PRELIMINARY AND WILL BE CONFIRMED DURING DETAIL DESIGN.

NOTES

1. FILTER CONTROL LOGIC BOX ORIGINATES ON P&ID 1000-PID-0003. THE BOX SHOWN ON THIS P&ID REPRESENTS THE SAME BOX.

NOT PUBLISHED. ALL RIGHTS RESERVED BY THE ENGINEER. DRAWINGS AND SPECIFICATIONS, AS INSTRUMENTS OF SERVICE, ARE ISSUED TO DESCRIBE DESIGN INTENT. THEY ARE NOT TO BE USED ON OTHER PROJECTS OR EXTENSIONS TO THIS PROJECT, EXCEPT BY AGREEMENT IN WRITING AND WITH APPROPRIATE COMPENSATION TO THE ENGINEER. CONTRACTOR, SUB-CONTRACTORS, AND SUPPLIERS ARE RESPONSIBLE FOR CONFIRMING AND CORRELATING DIMENSIONS AND CONDITIONS AT THE JOB SITE, AND SHALL NOTIFY THE ENGINEER IMMEDIATELY OF ANY ERRORS OR DISCREPANCIES IN REGARD TO SUCH DRAWINGS. DESCRIBING DESIGN INTENT, SHALL NOT INDICATE EVERY DETAIL OR SYSTEM FOR CONSTRUCTION. CONTRACTOR, SUB-CONTRACTORS, AND SUPPLIERS SHALL BE RESPONSIBLE TO PROVIDE ADDITIONAL DRAWINGS AS NECESSARY FOR PERMITS, ERECTION, INSTALLATION, AND COORDINATION OF ALL WORK. CONTRACTOR, SUB-CONTRACTORS, AND SUPPLIERS SHALL BE RESPONSIBLE FOR ALL LABOR AND MATERIALS REQUIRED IN ACCORDANCE WITH DESIGN INTENT. ALL MATERIALS SHALL BE NEW, UNLESS SPECIFIED OTHERWISE, AND SHALL BE INSTALLED LEVEL, PLUMB, STRAIGHT, AND TRUE TO LINE, IN ACCORDANCE WITH THE BEST PRACTICES OF THE TRADES. THE ENGINEER SHALL NOT BE RESPONSIBLE FOR CONSTRUCTION MEANS, METHODS, TECHNIQUES, SEQUENCES OR PROCEDURES, OR FOR SAFETY PRECAUTIONS AND PROGRAMS IN CONNECTION WITH THE WORK. ALL WORK SHALL BE PERFORMED IN ACCORDANCE WITH APPLICABLE CODES AND ORDINANCES.

REFERENCE DRAWINGS:		
REV #	DATE	DESCRIPTION
A	12/5/2015	ISSUED FOR INTERNAL REVIEW APPROVAL

REV #	DATE	DESCRIPTION	DRWN	CHKD	APVD
A	12/5/2015	ISSUED FOR INTERNAL REVIEW APPROVAL	GS	DLH	PDN

CLIENT: MOTIVA ENTERPRISES LLC
PLANT: PORT ARTHUR REFINERY
JOB NO:

PIPING & INSTRUMENTATION DIAGRAM	
SAND FILTER A	
PROJ TITLE: AROMATICS UTILITY SCOPE REVIEW	

SSP ENGINEERING & CONSULTING		FIRM NUMBER #13619
PROJECT NO: 25MA02	SCALE: NONE	
DRAWN BY: GS	CHECKED: APB	
DESIGN BY:	ENG APVL: PDN	
DRAWING NO: 1000-PID-0001		REV A

[illegible]